




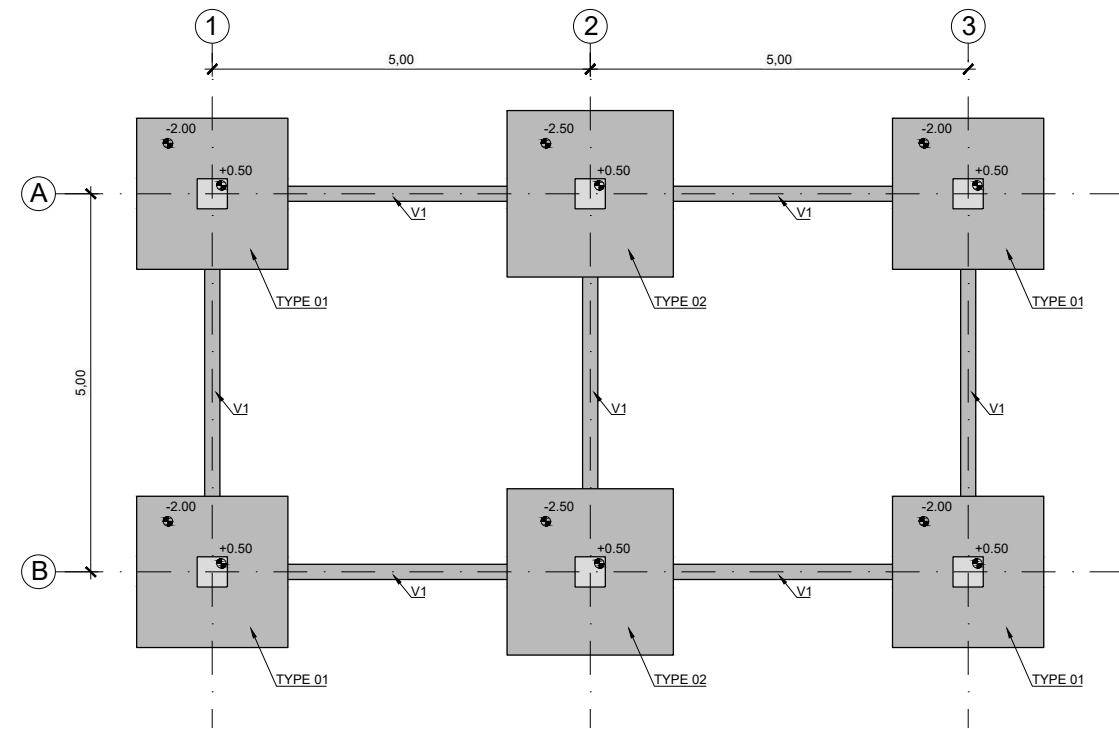


PLAN VIEW
SCALE 1:50

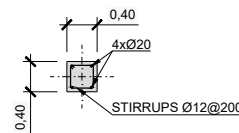


SECTION B-B
SCALE 1:50

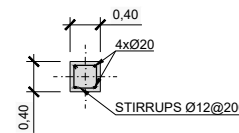


SECTION B-B
SCALE 1:50

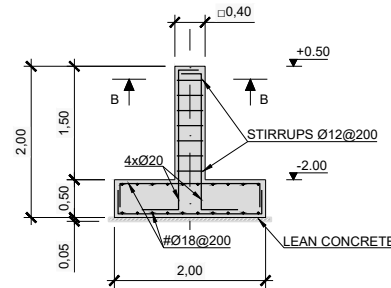


SECTION A-A
SCALE 1:50

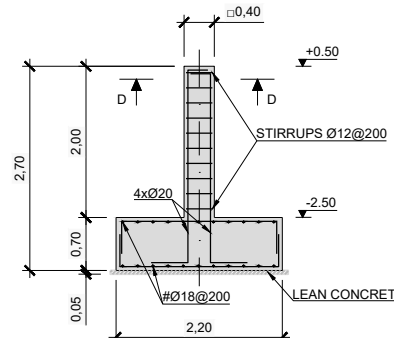


SECTION C-C
SCALE 1:50

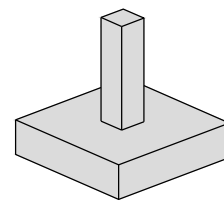


TYPE 01
3D VIEW

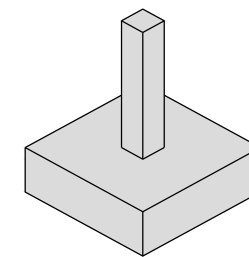


TYPE 02
3D VIEW

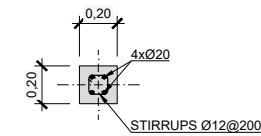

V1
SCALE 1:20

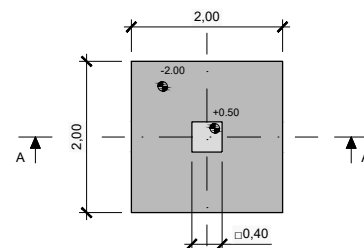

TYPE 01 PLAN VIEW
SCALE 1:50

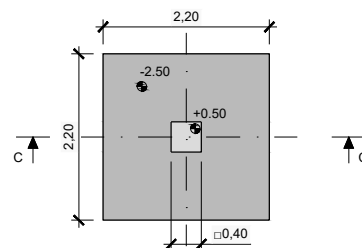

TYPE 02 PLAN VIEW
SCALE 1:50

PROJECT Title: PERSONAL PROJECT Code:	AUTOR	SCALE 1:200 Numerical	DATE SEPTEMBER 2025 Graph Original UNE A-1	DRAWING TITLE Title: FOUNDATIONS PLAN Discipline:	NAME OF DRAWING DRAWING N° SHEET N° 1/1
--	--------------	--	--	--	--