




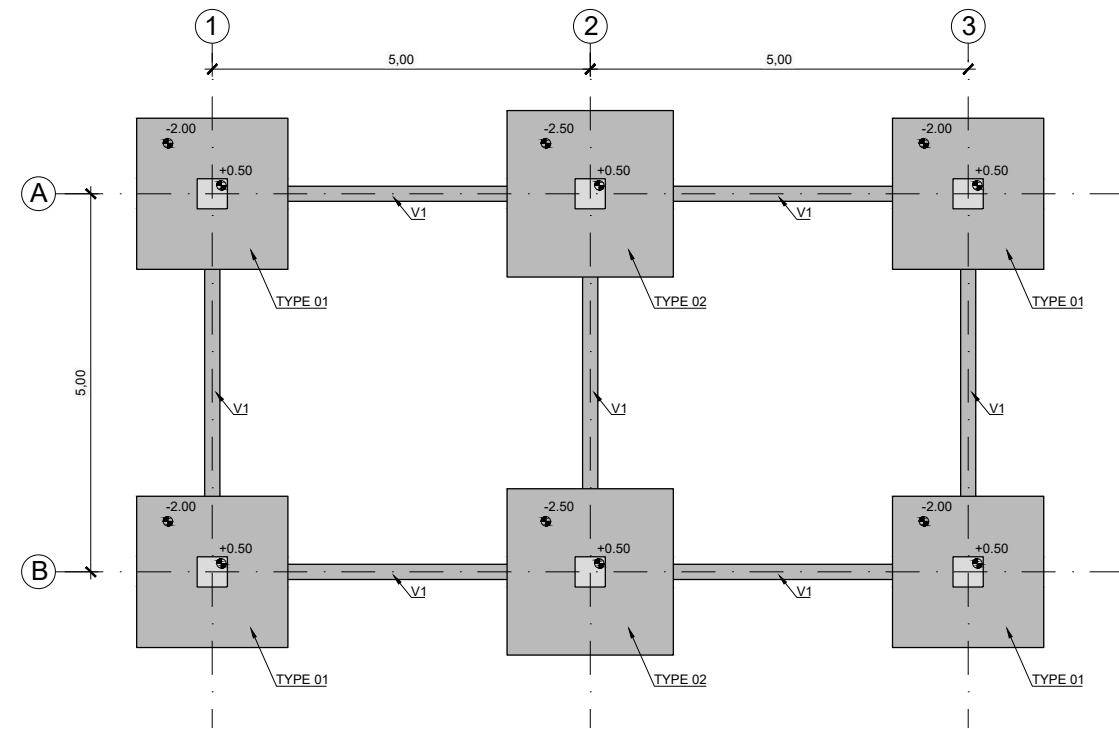


PLAN VIEW
SCALE 1:50

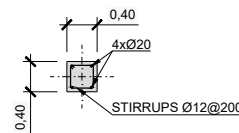


SECTION B-B
SCALE 1:50

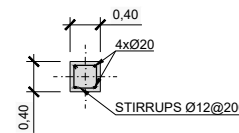


SECTION B-B
SCALE 1:50

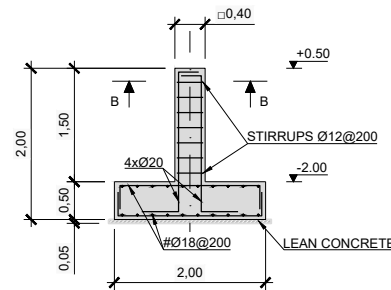


SECTION A-A
SCALE 1:50

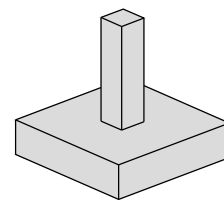


TYPE 01
3D VIEW

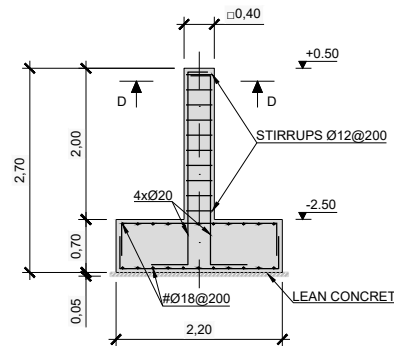


SECTION C-C
SCALE 1:50

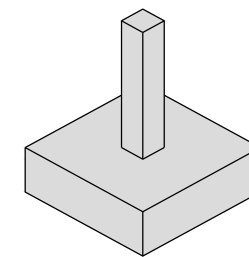


TYPE 02
3D VIEW

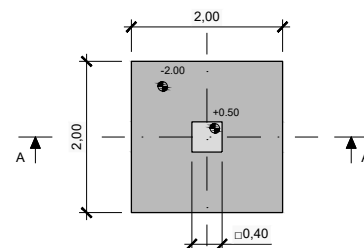

TYPE 01 PLAN VIEW
SCALE 1:50

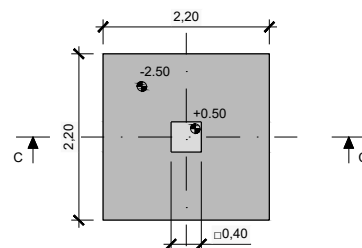

TYPE 02 PLAN VIEW
SCALE 1:50

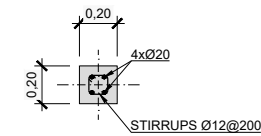

V1
SCALE 1:20

	PROJECT Title: PERSONAL PROJECT Code:	AUTOR MIKEL BALIÑO ZUAZO	SCALE 1:200 Numerical Graph Original UNE A-1	DATE SEPTEMBER 2025	DRAWING TITLE Title: FOUNDATIONS PLAN Discipline:	NAME OF DRAWING DRAWING Nº SHEET Nº 1/1
--	--	-----------------------------	--	------------------------	--	--